


SHAFT DRAWING

ALLOCATION TO ASSEMBLIES	
Assembly Mark	TOTAL
B/971	1
Total	1

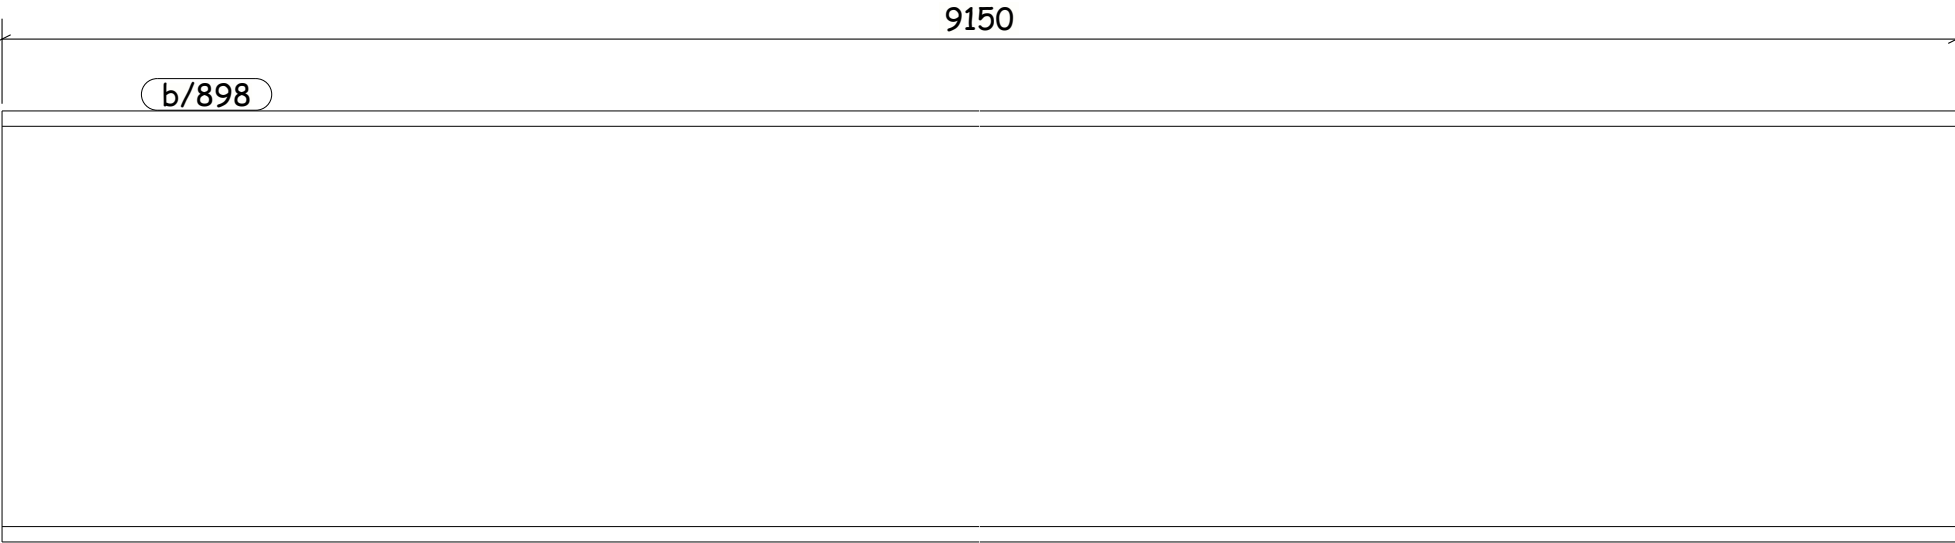

1 No BEAM REQUIRED AS DRAWN MARKED b/898

LOT	0	QTY	1
PHASE	1	QTY	1

Rev	By	Date	Details				
b/898		IPE300	S235JR	1	9150.4	10.61	372.7
Mark		Profile	Grade	QTY	Length	Area	Weight

Fabricación: HcB Ingeniería	
Project: CTIB 2026	
General Notes: ALL HOLES 22 Dia UNO FINISH: 0 Steel Grade: S235JR	Drawn:
	Checked:
	Scale: N.T.S.

Job No. /	Dwg No. /	Rev	A4
1 /	b/898 /		