
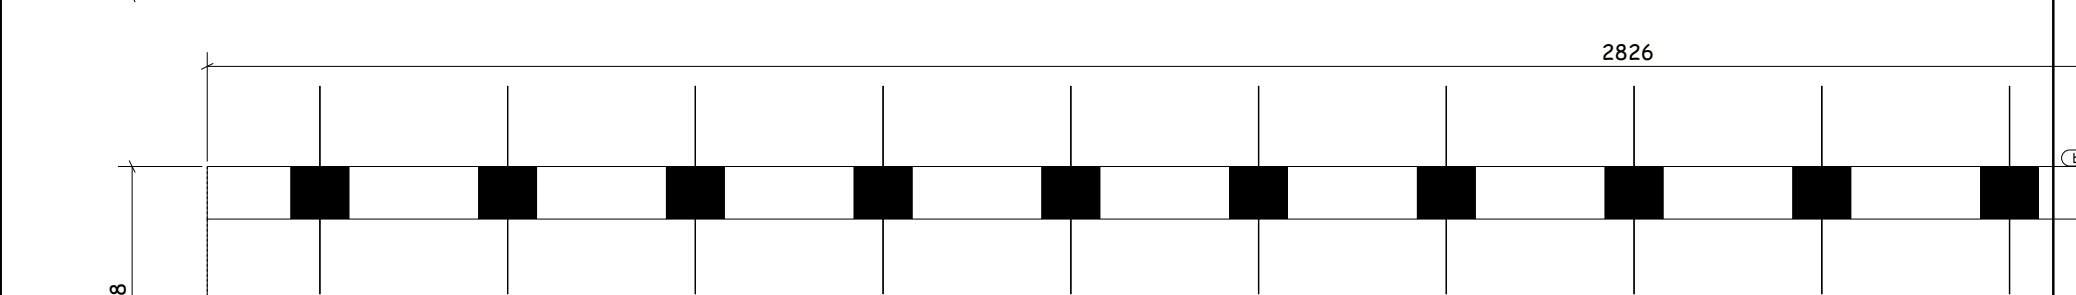


SHAFT DRAWING

ALLOCATION TO ASSEMBLIES

Assembly	TOTAL
75 <	
A/52	1
A/118	1
Total	2

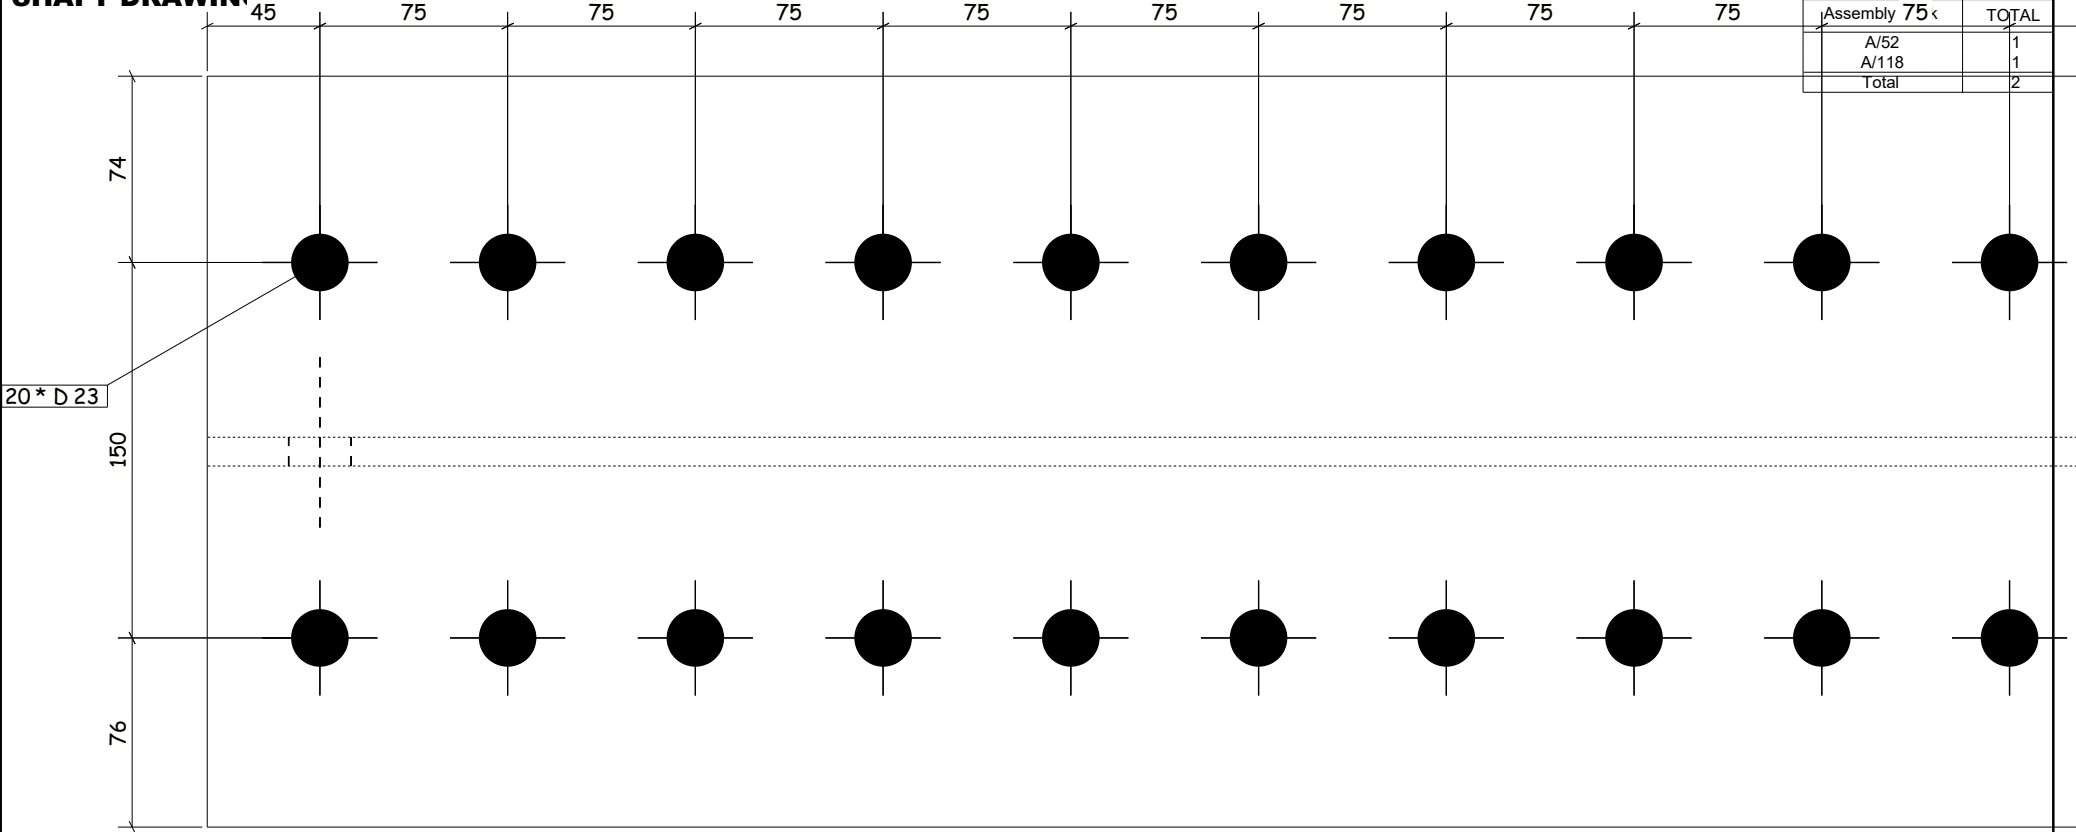

2 No BEAM REQUIRED AS DRAWN MARKED b/9

LOT	0	QTY	2
PHASE	1	QTY	2

Fabricación: HcB Ingeniería

Project: CTIB 2026

General Notes:

ALL HOLES 22 Dia UNO

FINISH: 0

Steel Grade: S235JR

Drawn:

Checked:

Scale: N.T.S.

HcB CTIB

Job No. / Dwg No. / Rev

1 / b/9 /

Tekla structures

Rev	By	Date	Details					
b/9			HEA450	S235JR	2	2825.6	5.68	381.0
Mark			Profile	Grade	QTY	Length	Area	Weight

4 * D.25