


SHAFT DRAWING

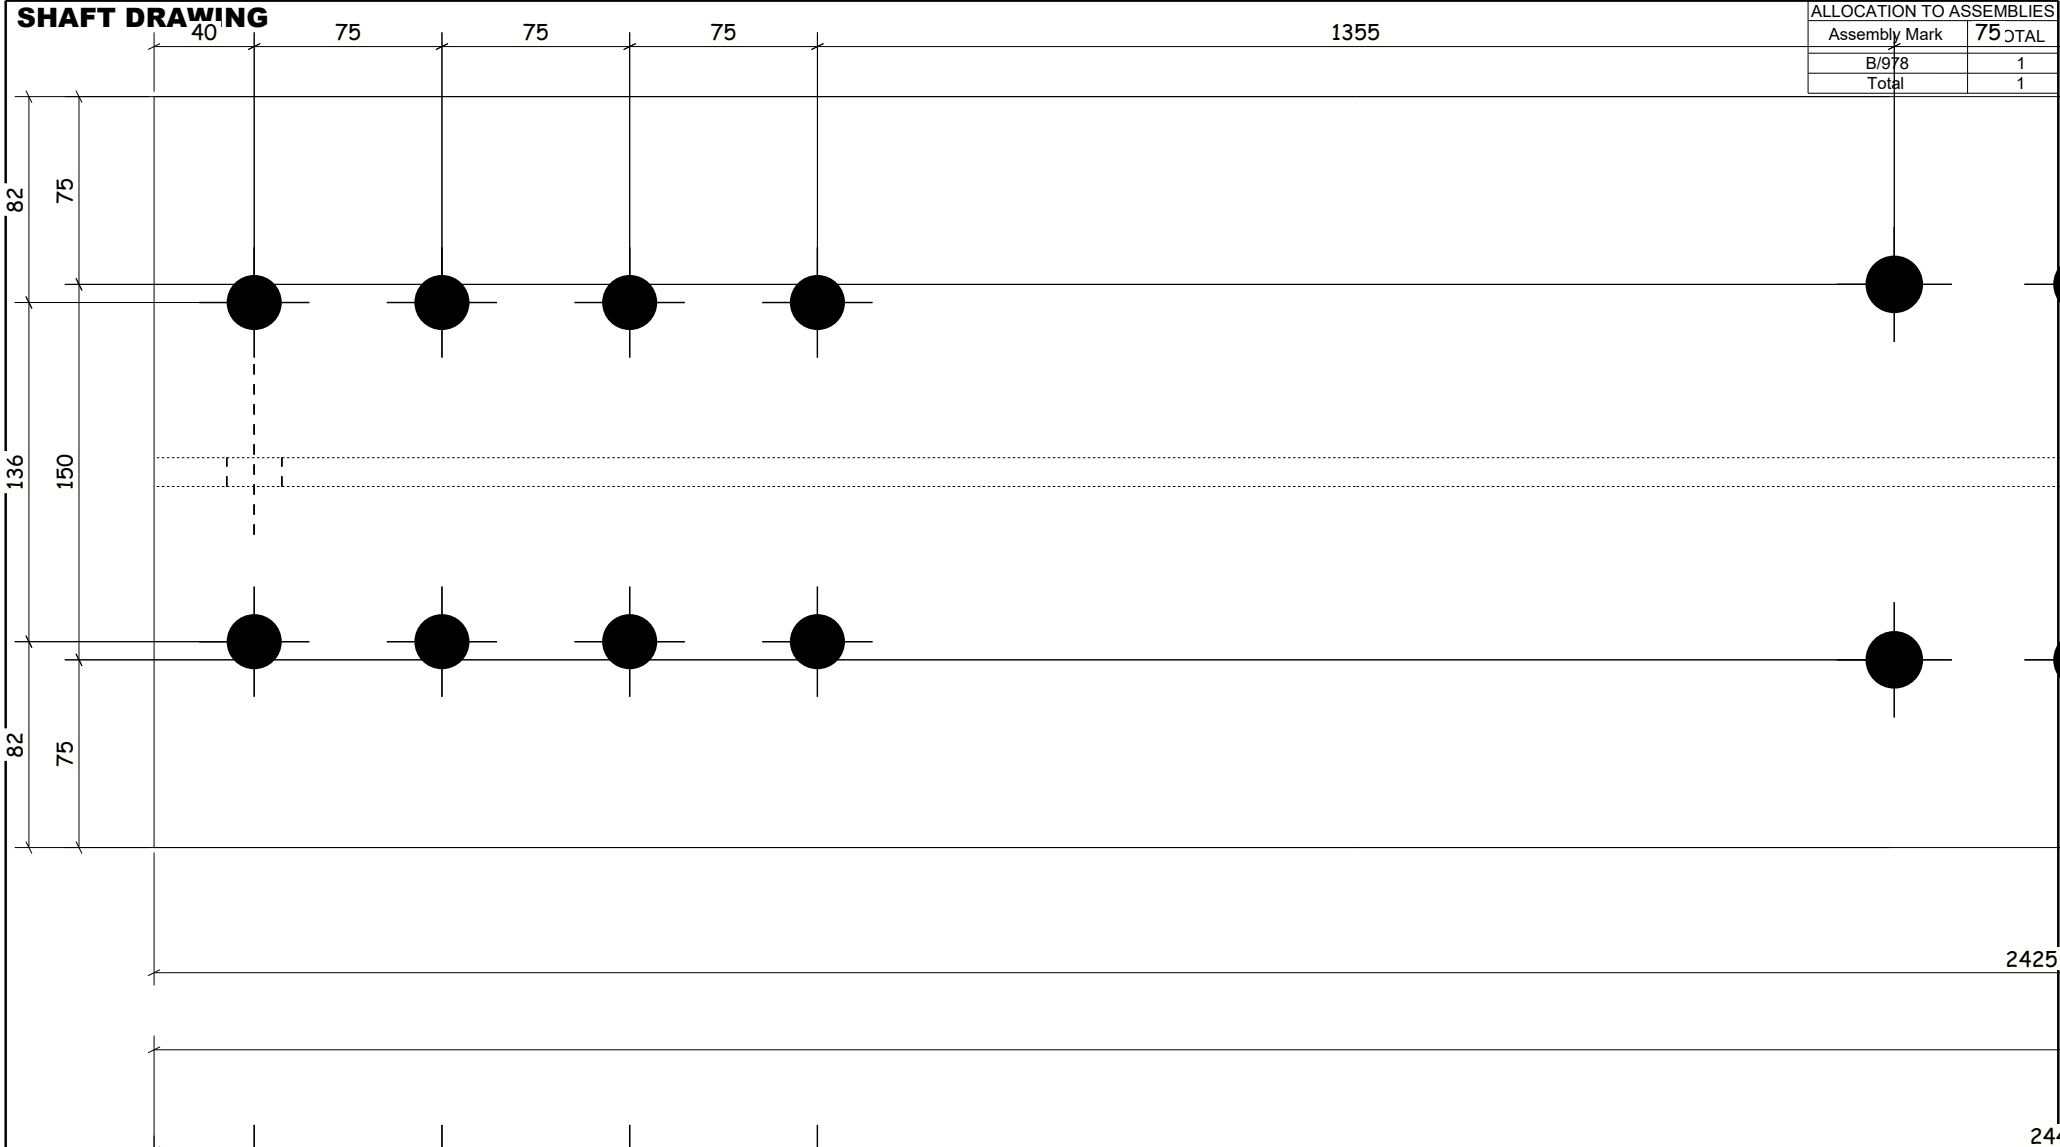

2425

2484

2444

1 No BEAM

REQUIRED AS DRAWN MARKED b/906

LOT	0	QTY	1
PHASE	1	QTY	1

b/906

Fabricación: HcB Ingeniería

Project: CTIB 2026

General Notes:

ALL HOLES 22 Dia UNO

FINISH: 0

Steel Grade: S235JR

Drawn:

Checked:

Scale: N.T.S.

HcB CTIB

Job No. / Dwg No. / Rev

1 / b/906 /

Tekla structures

108