


SHAFT DRAWING

ALLOCATION TO ASSEMBLIES	
Assembly Mark	TOTAL
B/985	3
Total	3

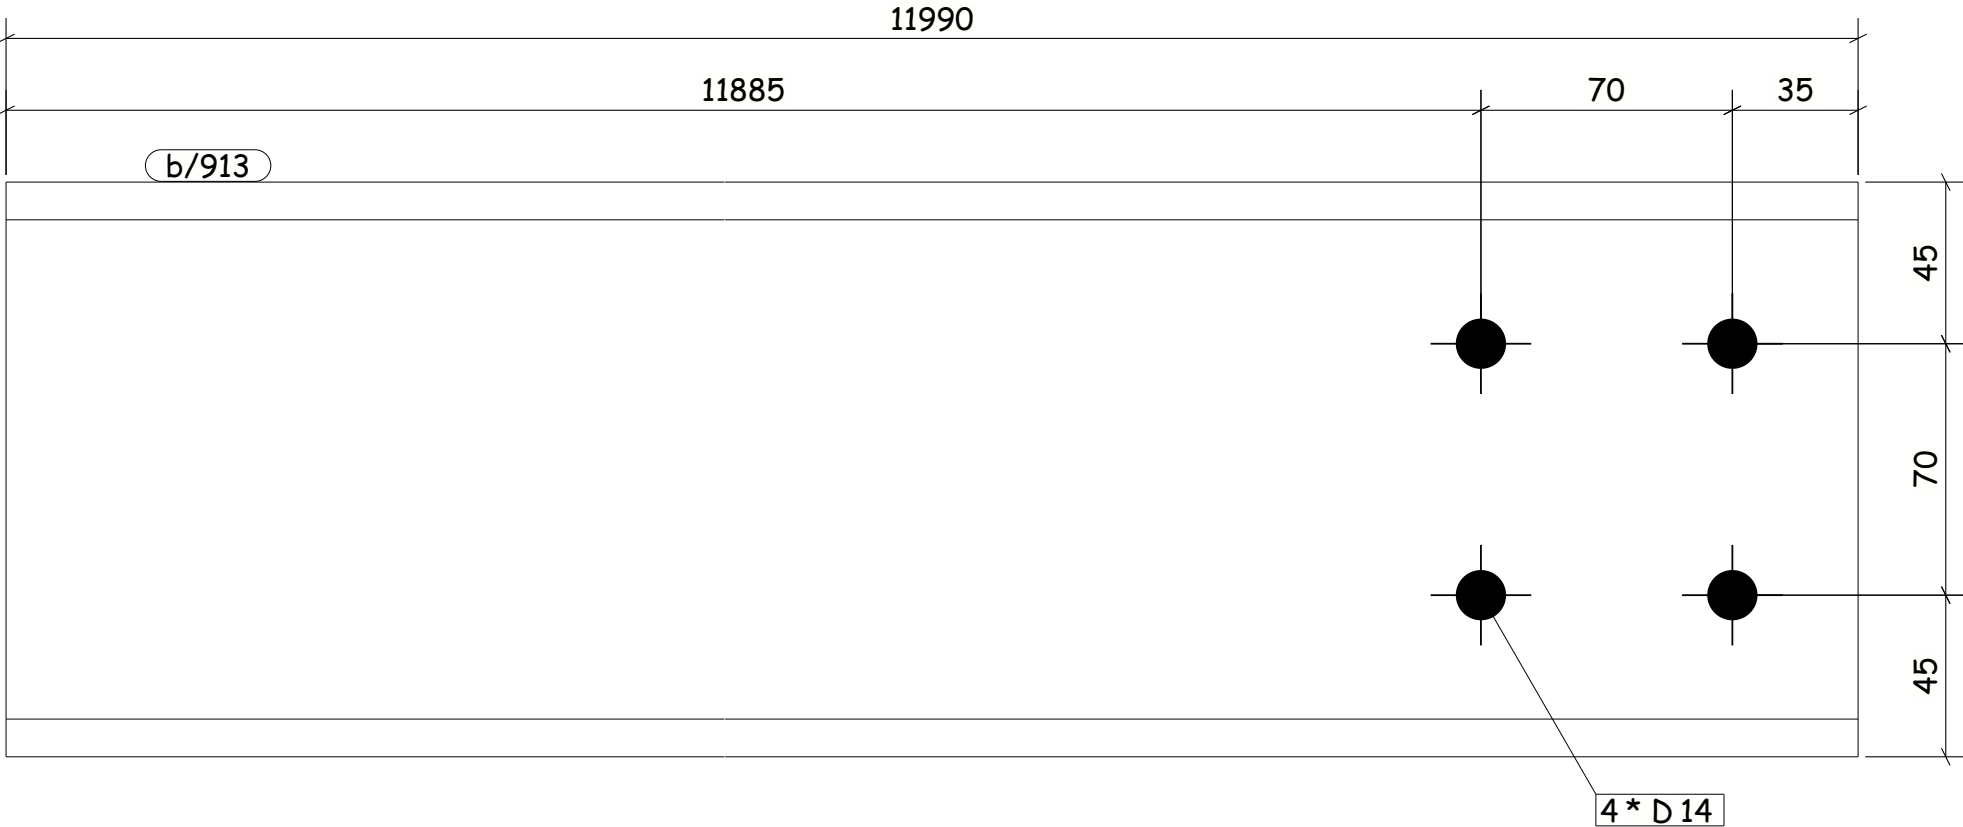

3 No BEAM

REQUIRED AS DRAWN MARKED b/913

LOT	0	QTY	3
PHASE	1	QTY	3

Rev	By	Date	Details				
b/913		UPN160	S235JR	3	11990.0	6.59	226.6
Mark		Profile	Grade	QTY	Length	Area	Weight

Fabricación: HcB Ingeniería

Project: CTIB 2026

General Notes:

ALL HOLES 22 Dia UNO

FINISH: 0

Steel Grade: S235JR

Drawn:

Checked:

Scale: N.T.S.

HcB CTIB

Job No. / Dwg No. / Rev

1 / b/913 /

A4