


SHAFT DRAWING

ALLOCATION TO ASSEMBLIES	
Assembly Mark	TOTAL
B/987	1
B/989	2
B/1061	1
B/1062	2
B/1065	1
B/1118	2
B/1119	1
B/1121	1
C/2	1
Total	12

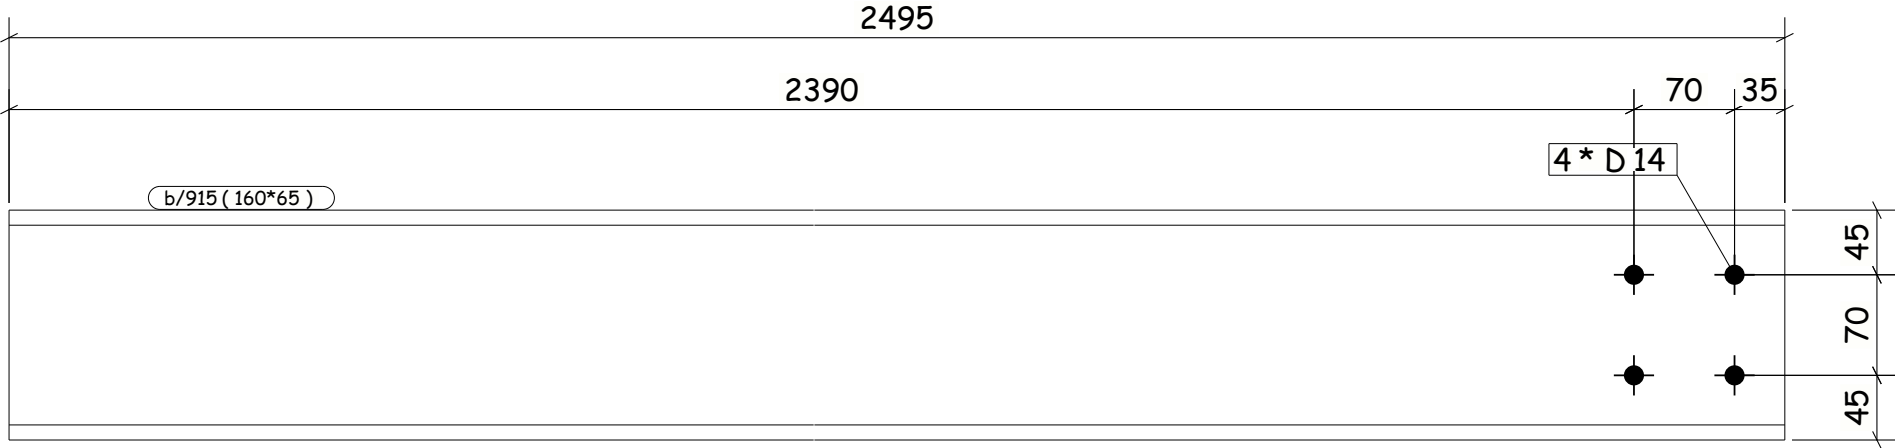

12 No BEAM

REQUIRED AS DRAWN MARKED b/915

LOT	0	QTY	12
PHASE	1	QTY	12

Rev	By	Date	Details				
b/915		UPN160	S235JR	12	2495.0	1.37	47.2
Mark		Profile	Grade	QTY	Length	Area	Weight

Fabricación: HcB Ingeniería

Project: CTIB 2026

General Notes:

ALL HOLES 22 Dia UNO

FINISH: 0

Steel Grade: S235JR

Drawn:

Checked:

Scale: N.T.S.

HcB CTIB

Job No. / Dwg No. / Rev

1 / b/915 /

A4