


SHAFT DRAWING

ALLOCATION TO ASSEMBLIES	
Assembly Mark	TOTAL
B/944	2
Total	2

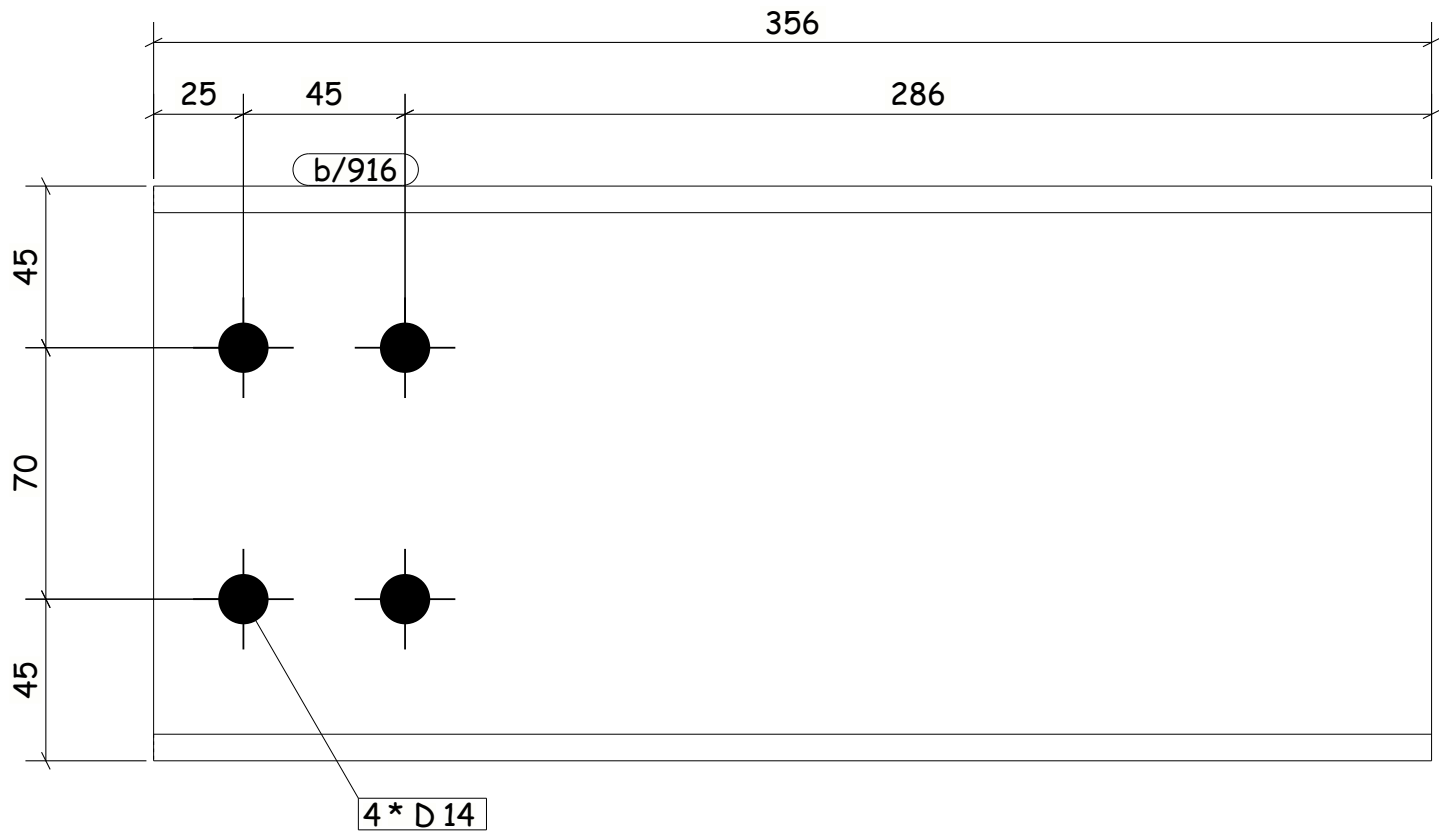

2 No BEAM

REQUIRED AS DRAWN MARKED b/916

LOT	0	QTY	2
PHASE	1	QTY	2

Rev	By	Date	Details				
b/916		IPE160	S235JR	2	355.8	0.22	5.4
Mark		Profile	Grade	QTY	Length	Area	Weight

Fabricación: HcB Ingeniería

Project: CTIB 2026

General Notes:

ALL HOLES 22 Dia UNO

FINISH: 0

Steel Grade: S235JR

Drawn:

Checked:

Scale: N.T.S.



Job No. / Dwg No. / Rev

1 / b/916 /

A4