


SHAFT DRAWING

ALLOCATION TO ASSEMBLIES	
Assembly Mark	TOTAL
B/216	1
Total	1

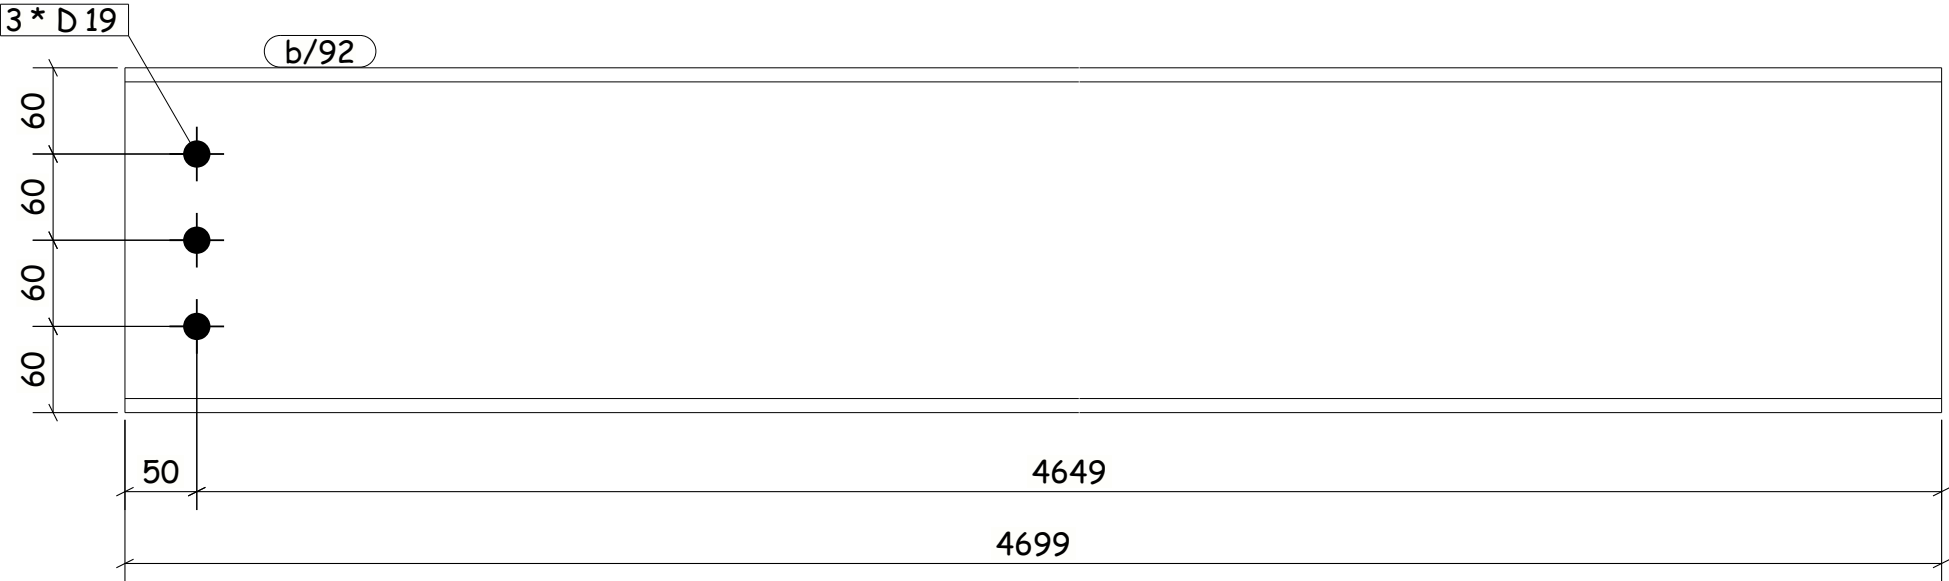

1 No BEAM REQUIRED AS DRAWN MARKED b/92

LOT	0	QTY	1
PHASE	1	QTY	1

Rev	By	Date	Details				
b/92		IPE240	S235JR	1	4698.8	4.33	137.2
Mark		Profile	Grade	QTY	Length	Area	Weight

Fabricación: HcB Ingeniería					
Project: CTIB 2026					
General Notes:	Drawn:				
ALL HOLES 22 Dia UNO	Checked:	Job No. /	Dwg No. /	Rev	A4
FINISH: 0	Scale: N.T.S.				
Steel Grade: S235JR		1 /	b/92	/	