


SHAFT DRAWING

ALLOCATION TO ASSEMBLIES	
Assembly Mark	TOTAL
B/82	2
B/959	1
B/974	3
Total	6

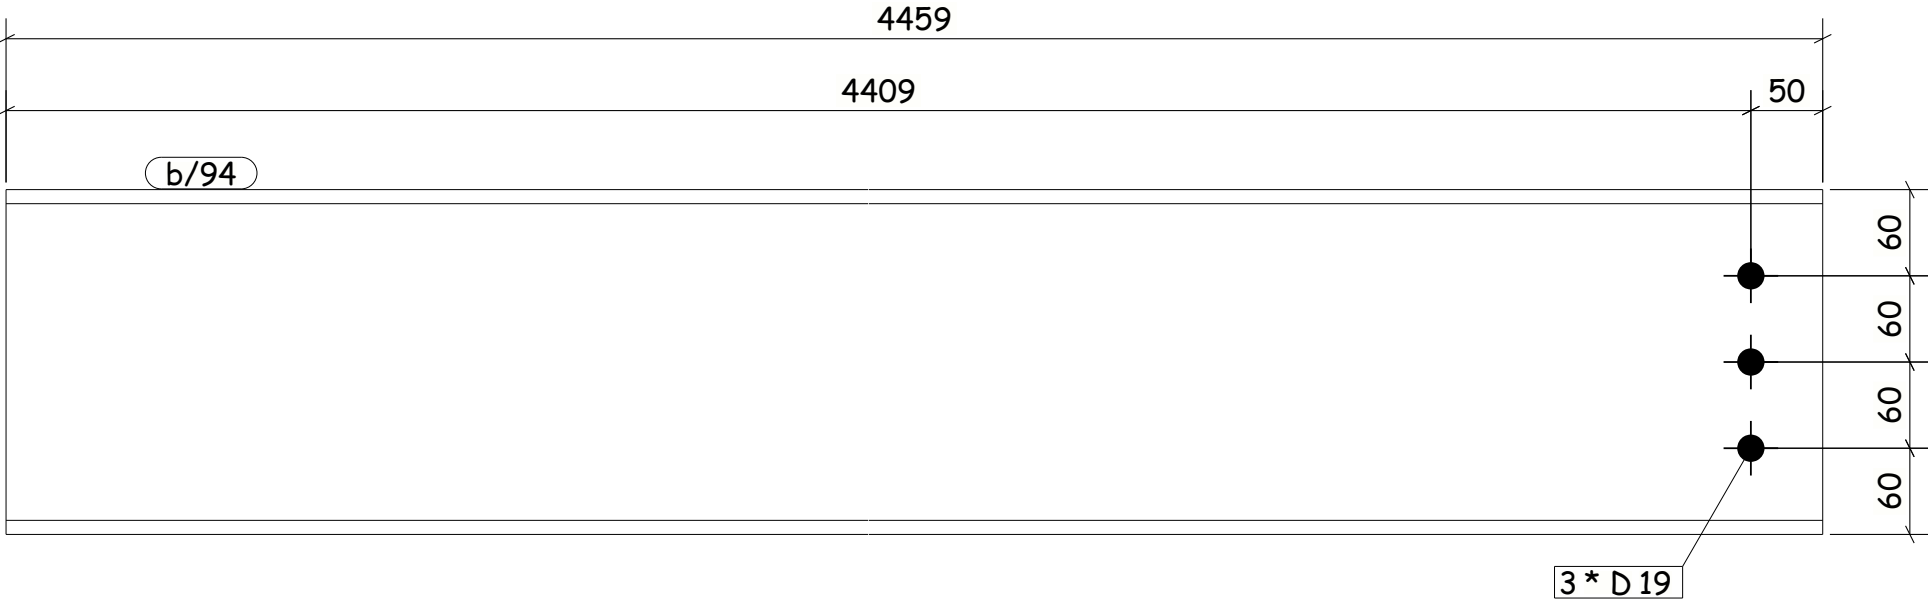

6 No BEAM

REQUIRED AS DRAWN MARKED b/94

LOT	0	QTY	6
PHASE	1	QTY	6

Rev	By	Date	Details				
b/94		IPE240	S235JR	6	4458.8	4.11	130.2
Mark		Profile	Grade	QTY	Length	Area	Weight

Fabricación: HcB Ingeniería

Project: CTIB 2026

General Notes:

ALL HOLES 22 Dia UNO

FINISH: 0

Steel Grade: S235JR

Drawn:

Checked:

Scale: N.T.S.

HcB CTIB

Job No. / Dwg No. / Rev

1 / b/94 /

A4