


SHAFT DRAWING

ALLOCATION TO ASSEMBLIES	
Assembly Mark	TOTAL
B/1081	4
B/1089	5
B/1287	3
C/2	3
Total	15

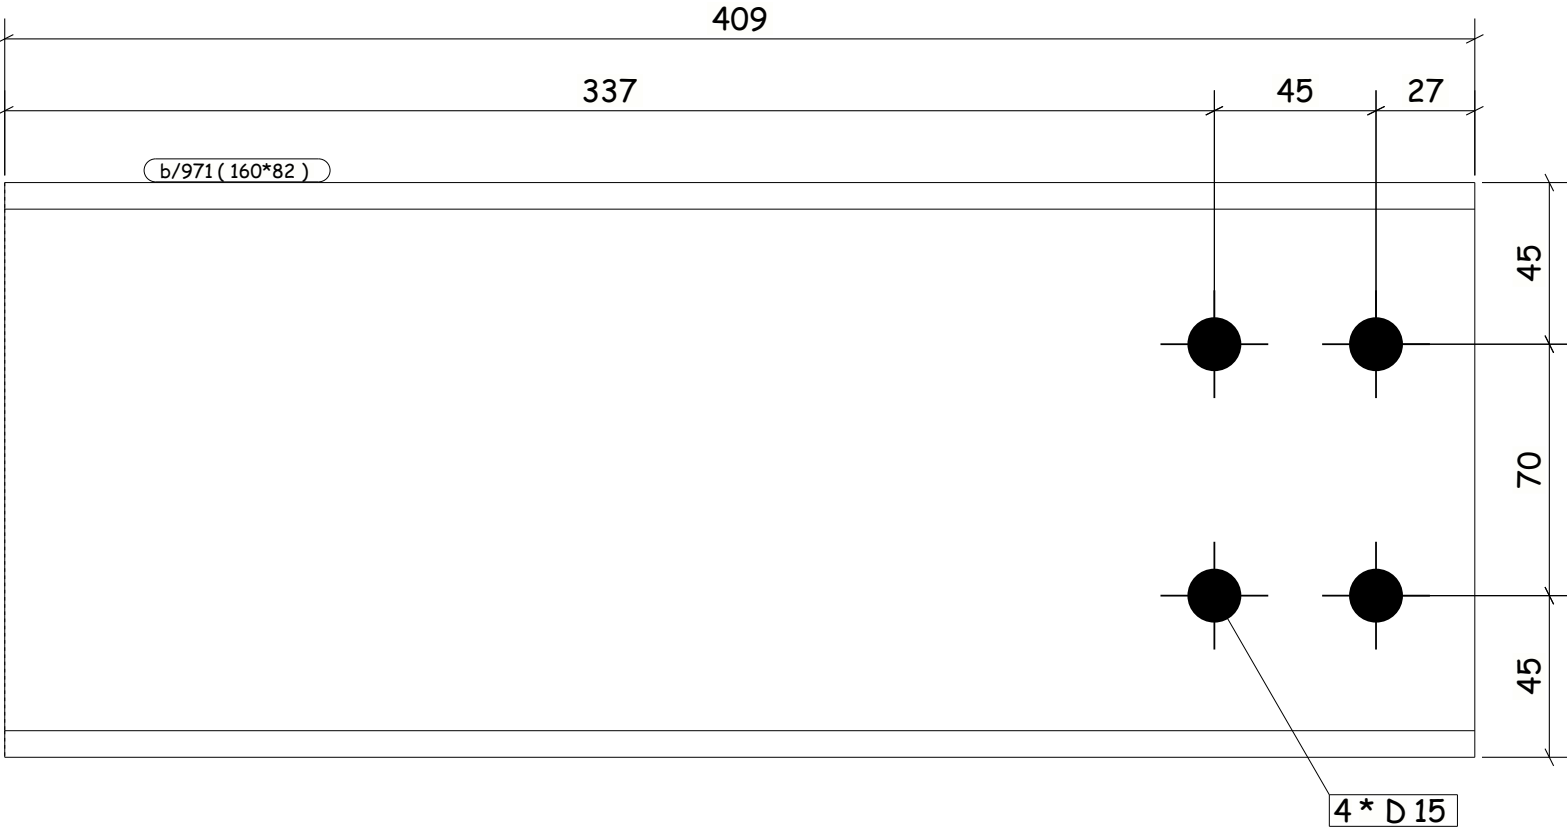

15 No BEAM

REQUIRED AS DRAWN MARKED b/971

LOT	0	QTY	15
PHASE	1	QTY	15

Rev	By	Date	Details				
b/971		IPE160	S235JR	15	409.3	0.25	6.2
Mark		Profile	Grade	QTY	Length	Area	Weight

Fabricación: HcB Ingeniería				
Project: CTIB 2026				
General Notes:	Drawn:			
ALL HOLES 22 Dia UNO	Checked:	Job No. / Dwg No. / Rev		A4
FINISH: 0	Scale: N.T.S.	1 / b/971 /		
Steel Grade: S235JR				